



Plano de construccion - rampa de 3 tramos (desnivel 136 cm, longitud 540 cm)

Vista a escala real (1 cm vertical = 1 cm horizontal)

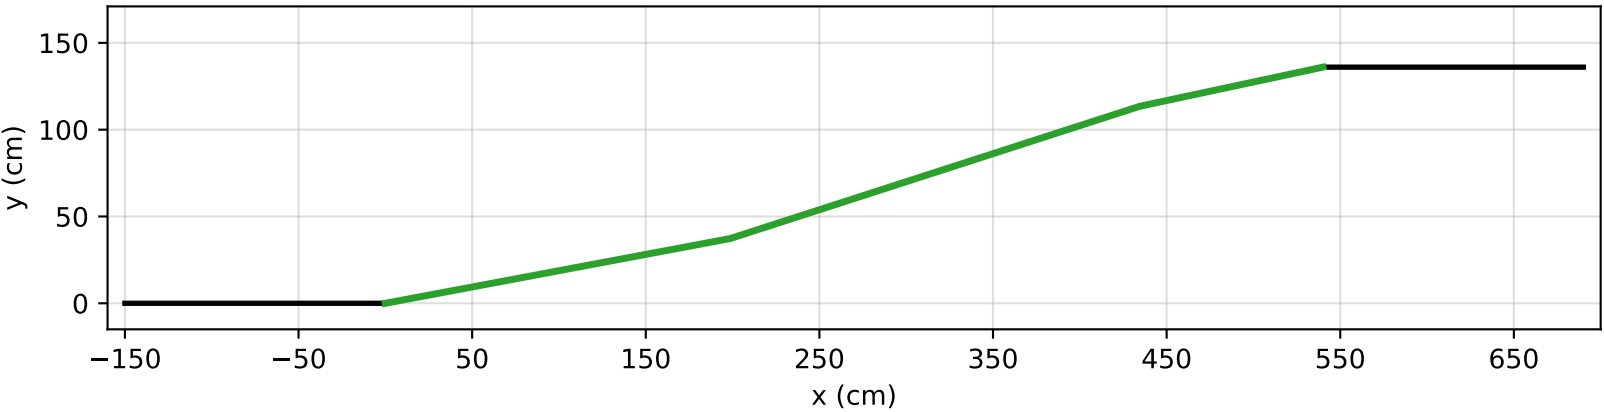

Plano de trabajo (escala vertical aumentada para mayor claridad) - usar los valores (x, y), no las proporciones visuales

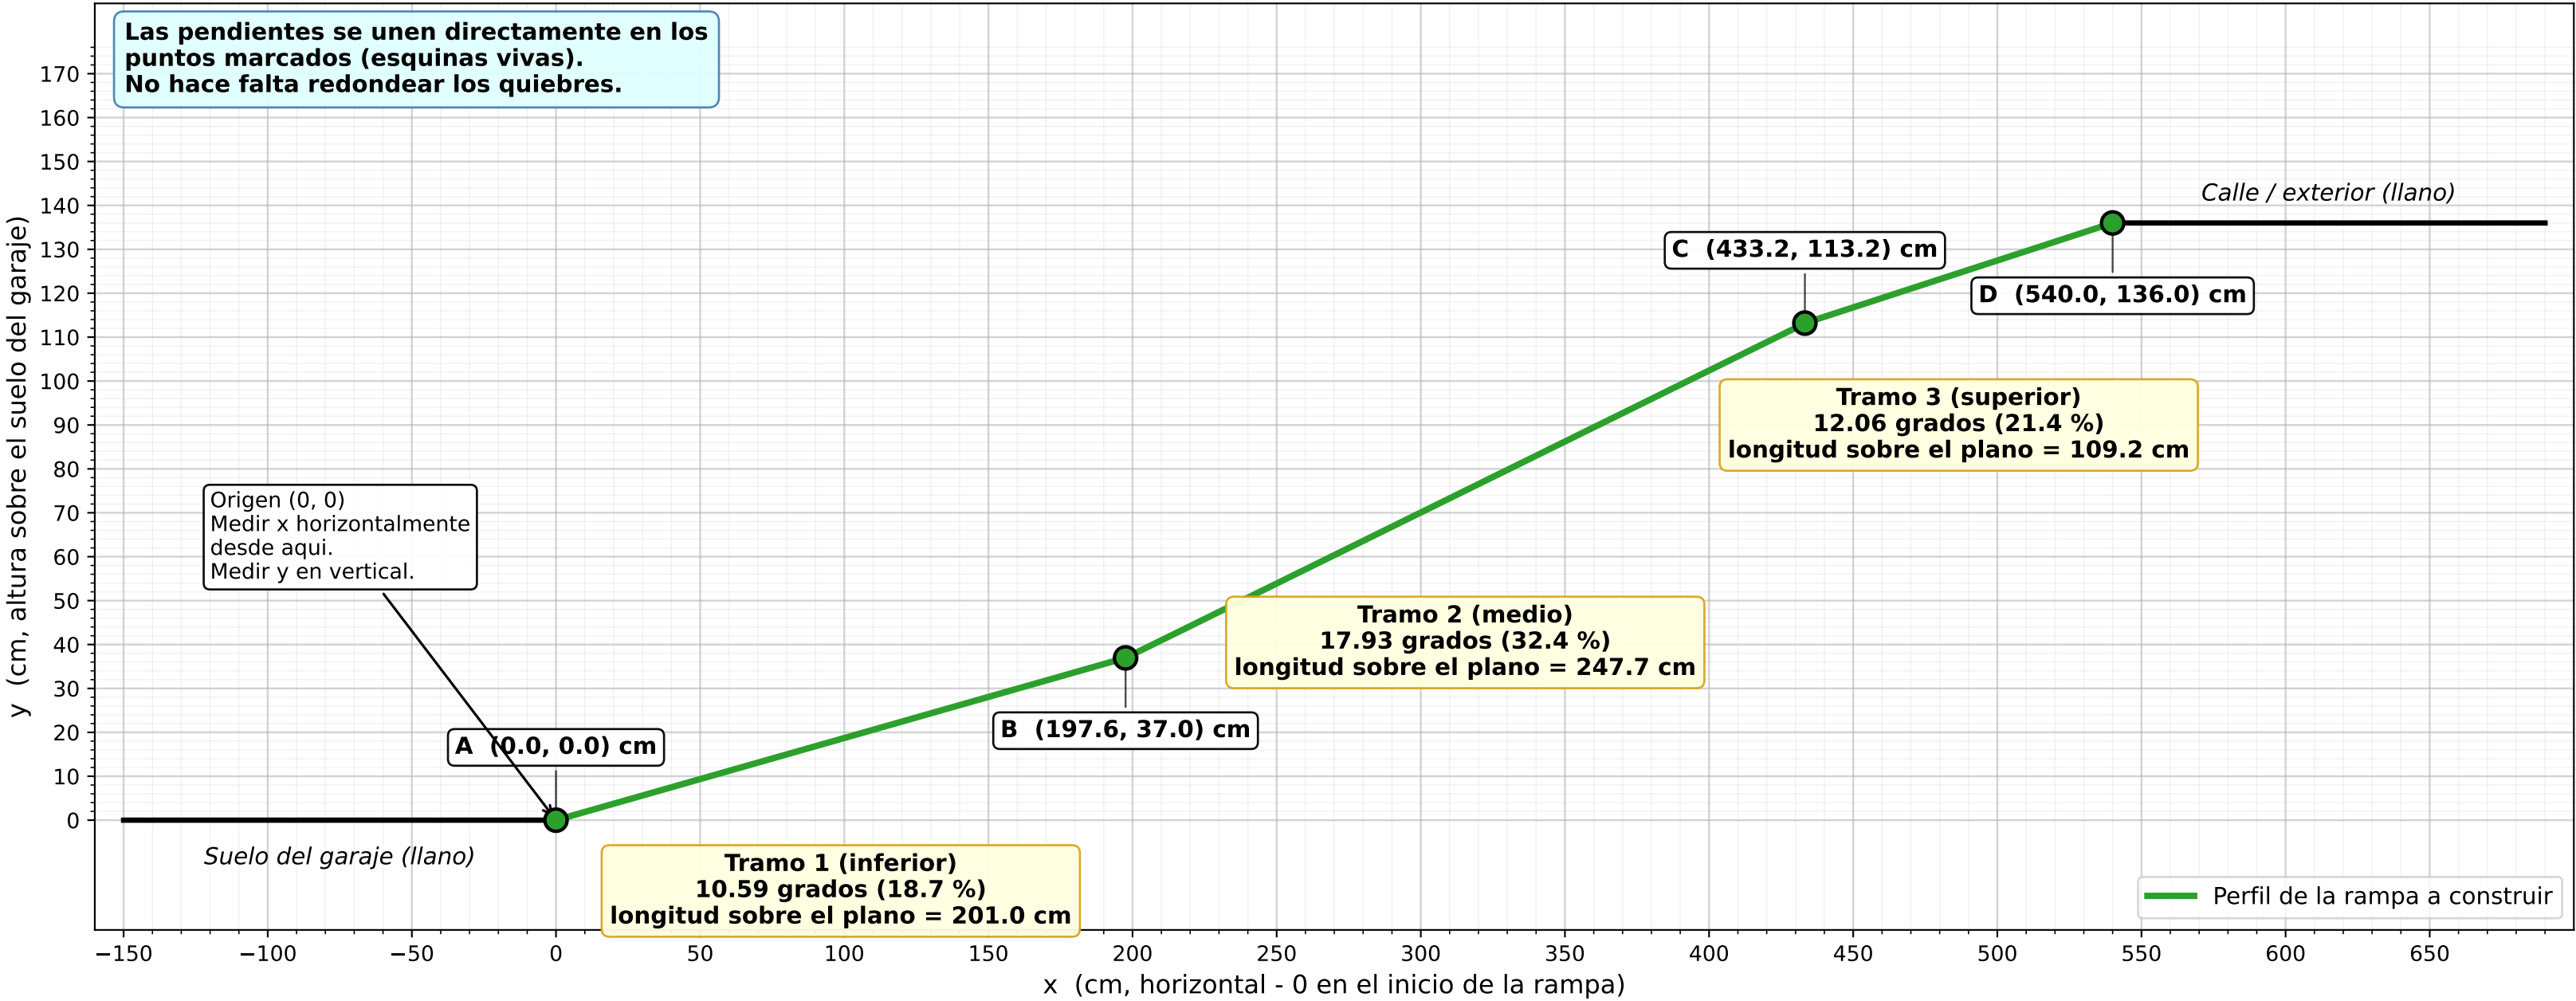

pt	que es	x (cm)	y (cm)	tipo
A	Inicio de la rampa (esquina)	0.0	0.0	esquina
B	Quiebre 1 (esquina teorica)	197.6	37.0	esquina
C	Quiebre 2 (esquina teorica)	433.2	113.2	esquina
D	Fin de la rampa (esquina)	540.0	136.0	esquina