
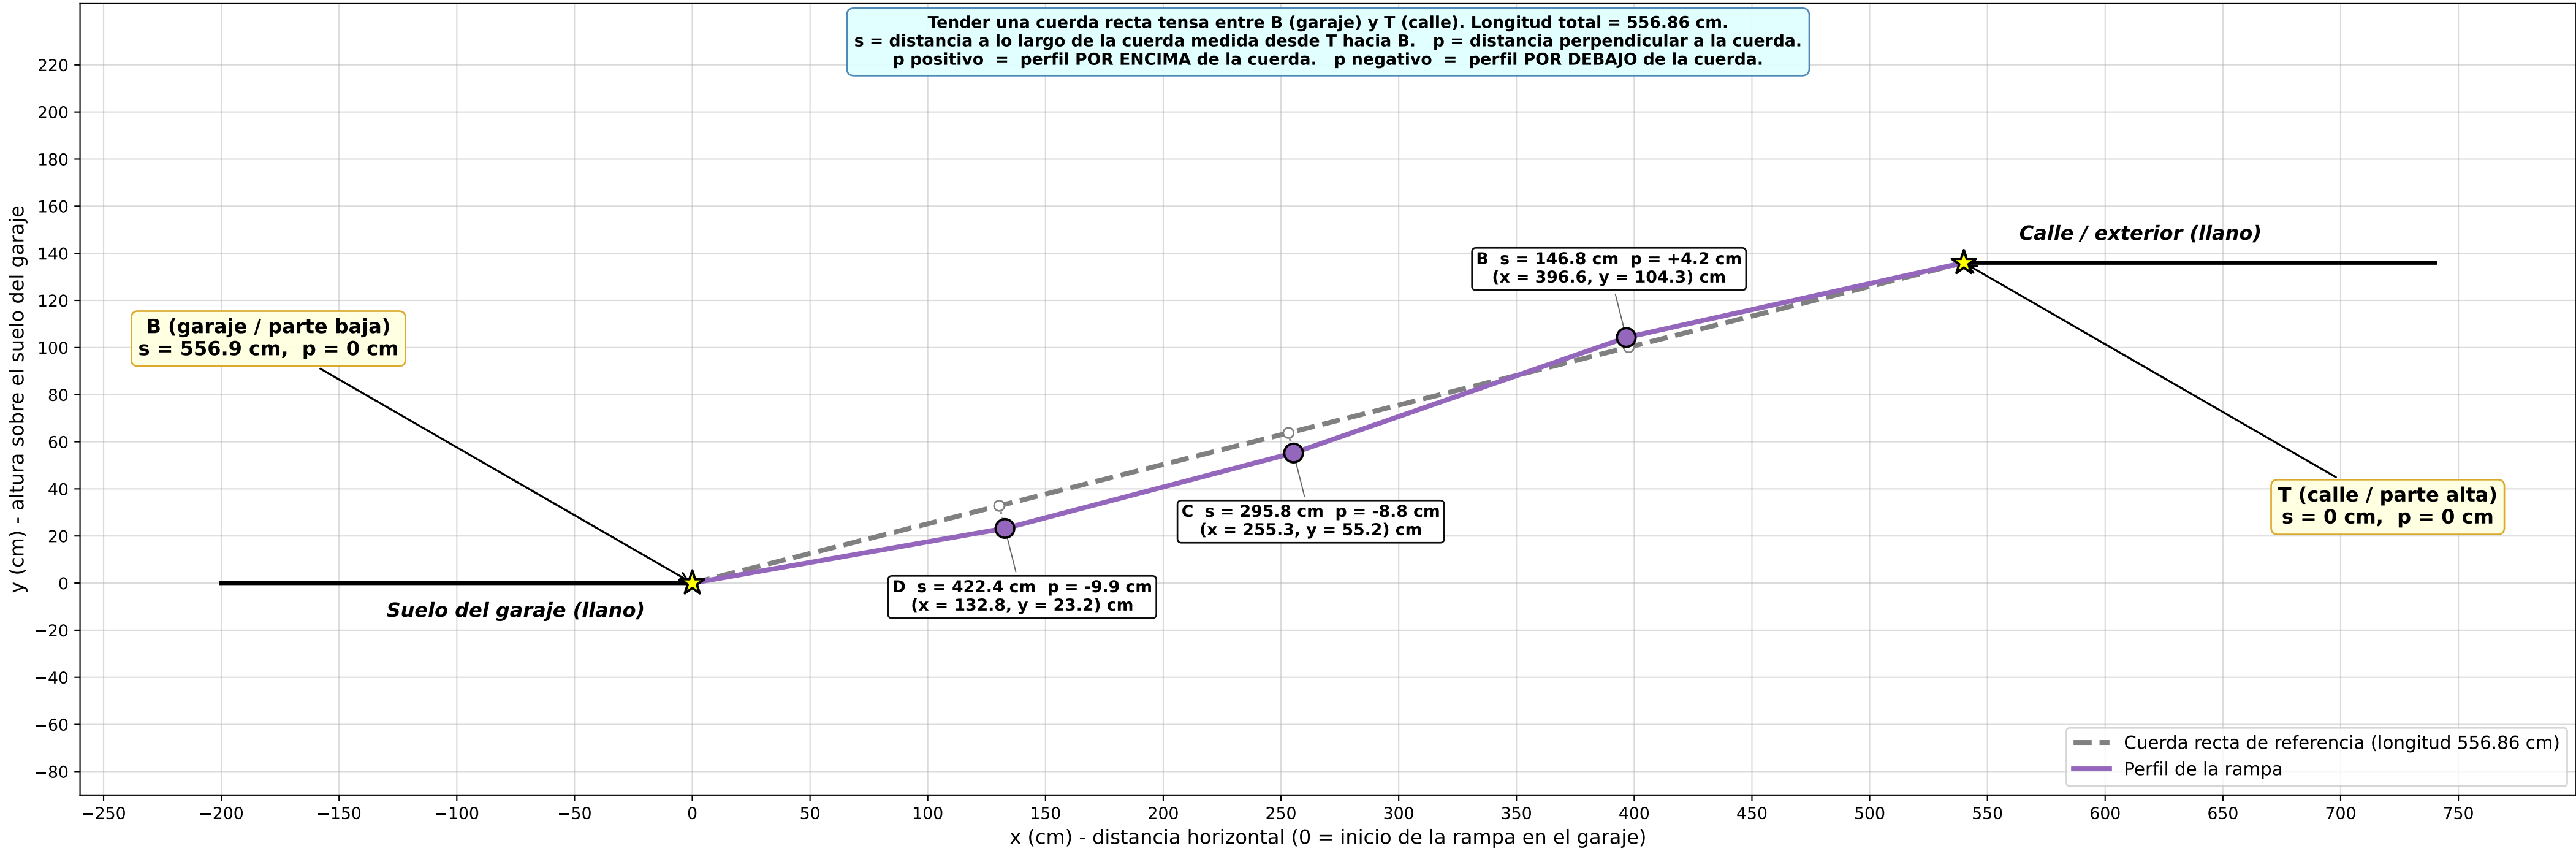


Plano de construccion (referencia: cuerda recta T → B) - rampa de 4 rectos (cuerda = 556.86 cm, desnivel 136 cm, longitud 540 cm)

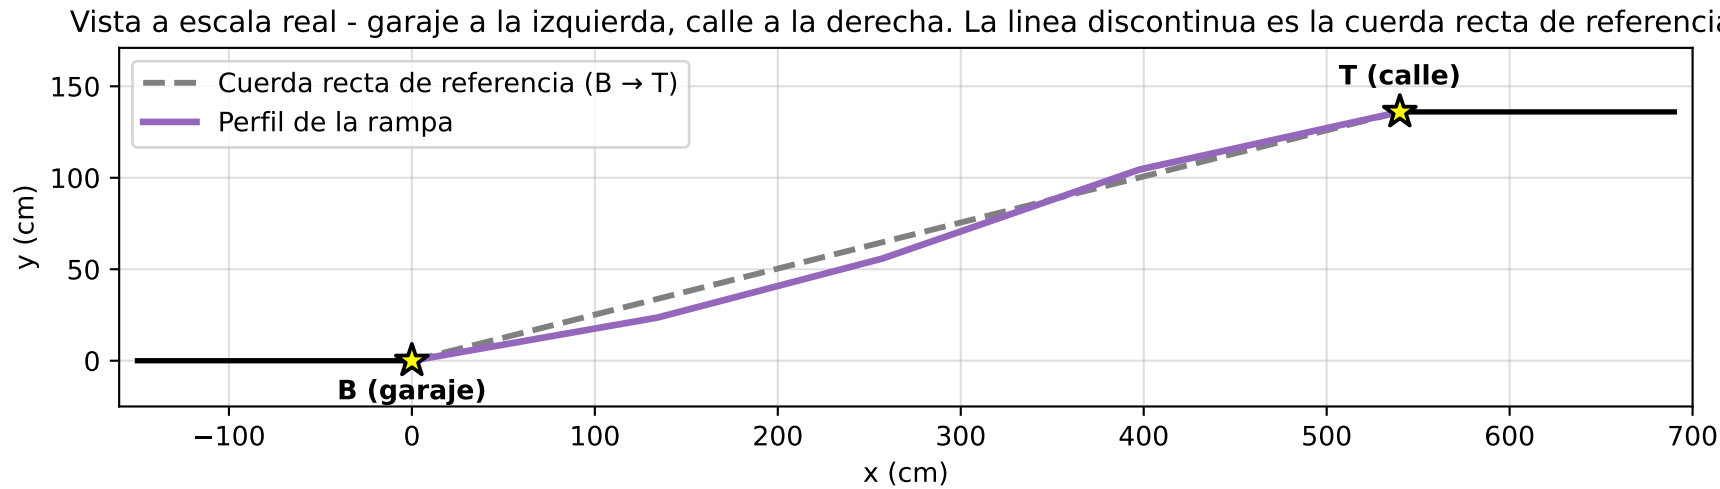

pt	que es	s (cm) along cuerda (desde T)	p (cm) perpendicular	x (cm) original	y (cm) original
A	Fin de la rampa (junto a la calle)	0.0	+0.0	540.0	136.0
B	Quiebre 3 (esquina)	146.8	+4.2	396.6	104.3
C	Quiebre 2 (esquina)	295.8	-8.8	255.3	55.2
D	Quiebre 1 (esquina)	422.4	-9.9	132.8	23.2
E	Inicio de la rampa (junto al garaje)	556.9	+0.0	0.0	0.0