
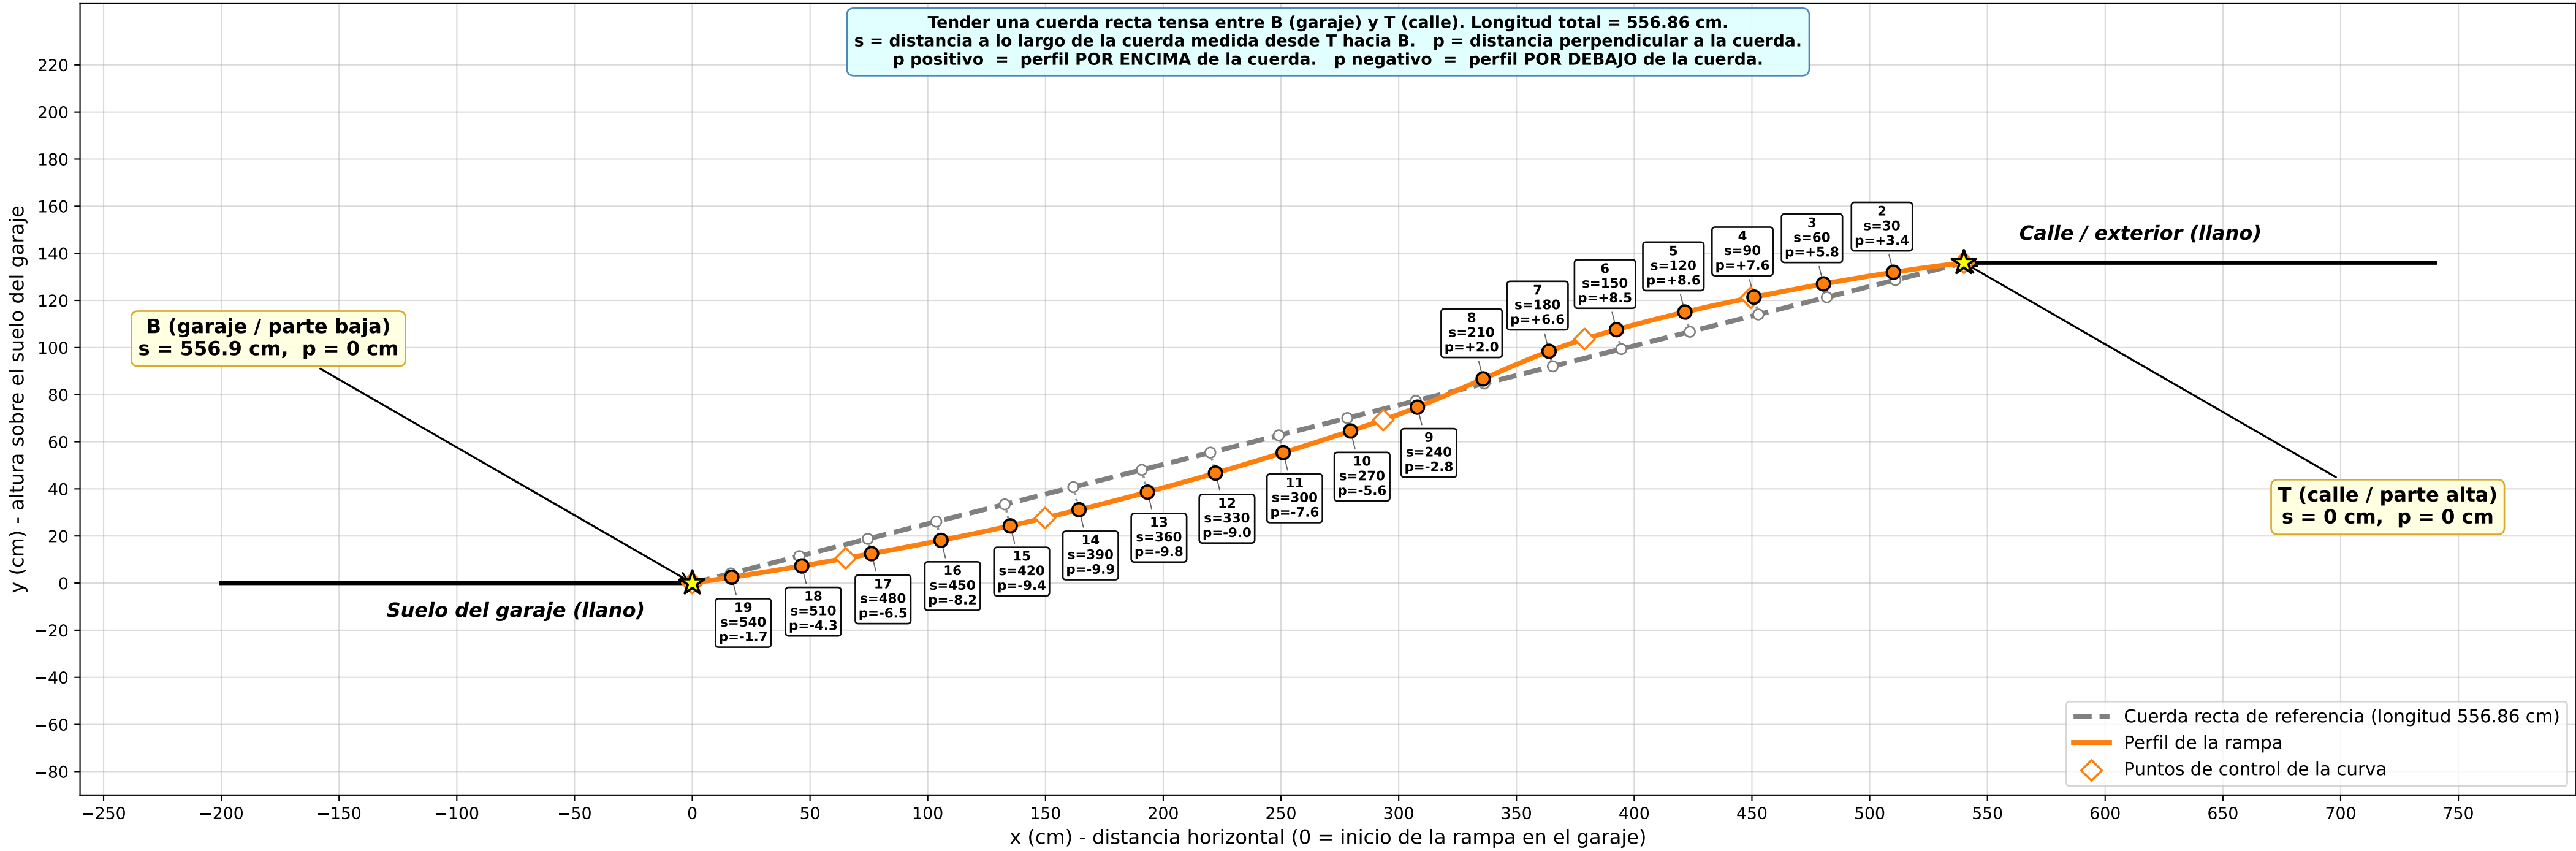


Plano de construccion (referencia: cuerda recta T → B) - curva suave libre (PCHIP) (cuerda = 556.86 cm, desnivel 136 cm, longitud 540 cm)

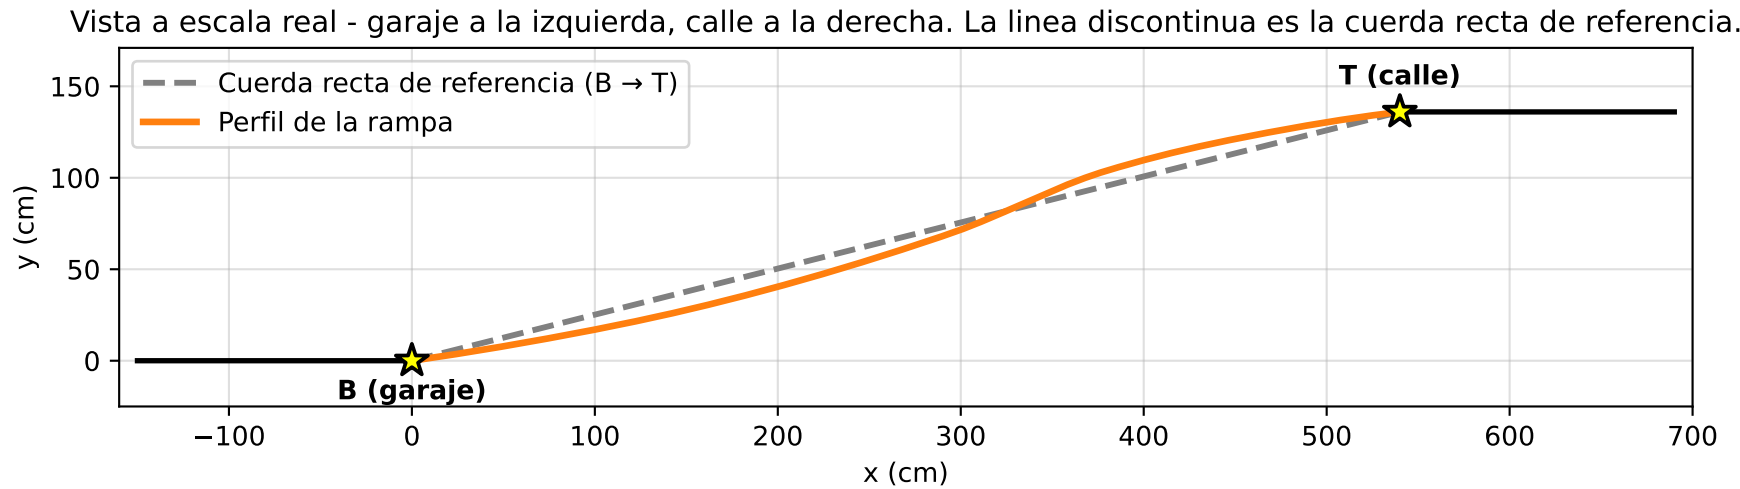

n	s (cm) along cuerda (desde T)	p (cm) perpendicular	tipo
1	0.0	+0.0	estacion superior (en T, junto a la calle)
2	30.0	+3.4	estacion intermedia
3	60.0	+5.8	estacion intermedia
4	90.0	+7.6	estacion intermedia
5	120.0	+8.6	estacion intermedia
6	150.0	+8.5	estacion intermedia
7	180.0	+6.6	estacion intermedia
8	210.0	+2.0	estacion intermedia
9	240.0	-2.8	estacion intermedia
10	270.0	-5.6	estacion intermedia
11	300.0	-7.6	estacion intermedia
12	330.0	-9.0	estacion intermedia
13	360.0	-9.8	estacion intermedia
14	390.0	-9.9	estacion intermedia
15	420.0	-9.4	estacion intermedia
16	450.0	-8.2	estacion intermedia
17	480.0	-6.5	estacion intermedia
18	510.0	-4.3	estacion intermedia
19	540.0	-1.7	estacion intermedia
20	556.9	-0.0	estacion inferior (en B, junto al garaje)