


Plano de construccion (referencia: muro y plano superior) - rampa de 3 tramos (desnivel 136 cm, longitud 540 cm)

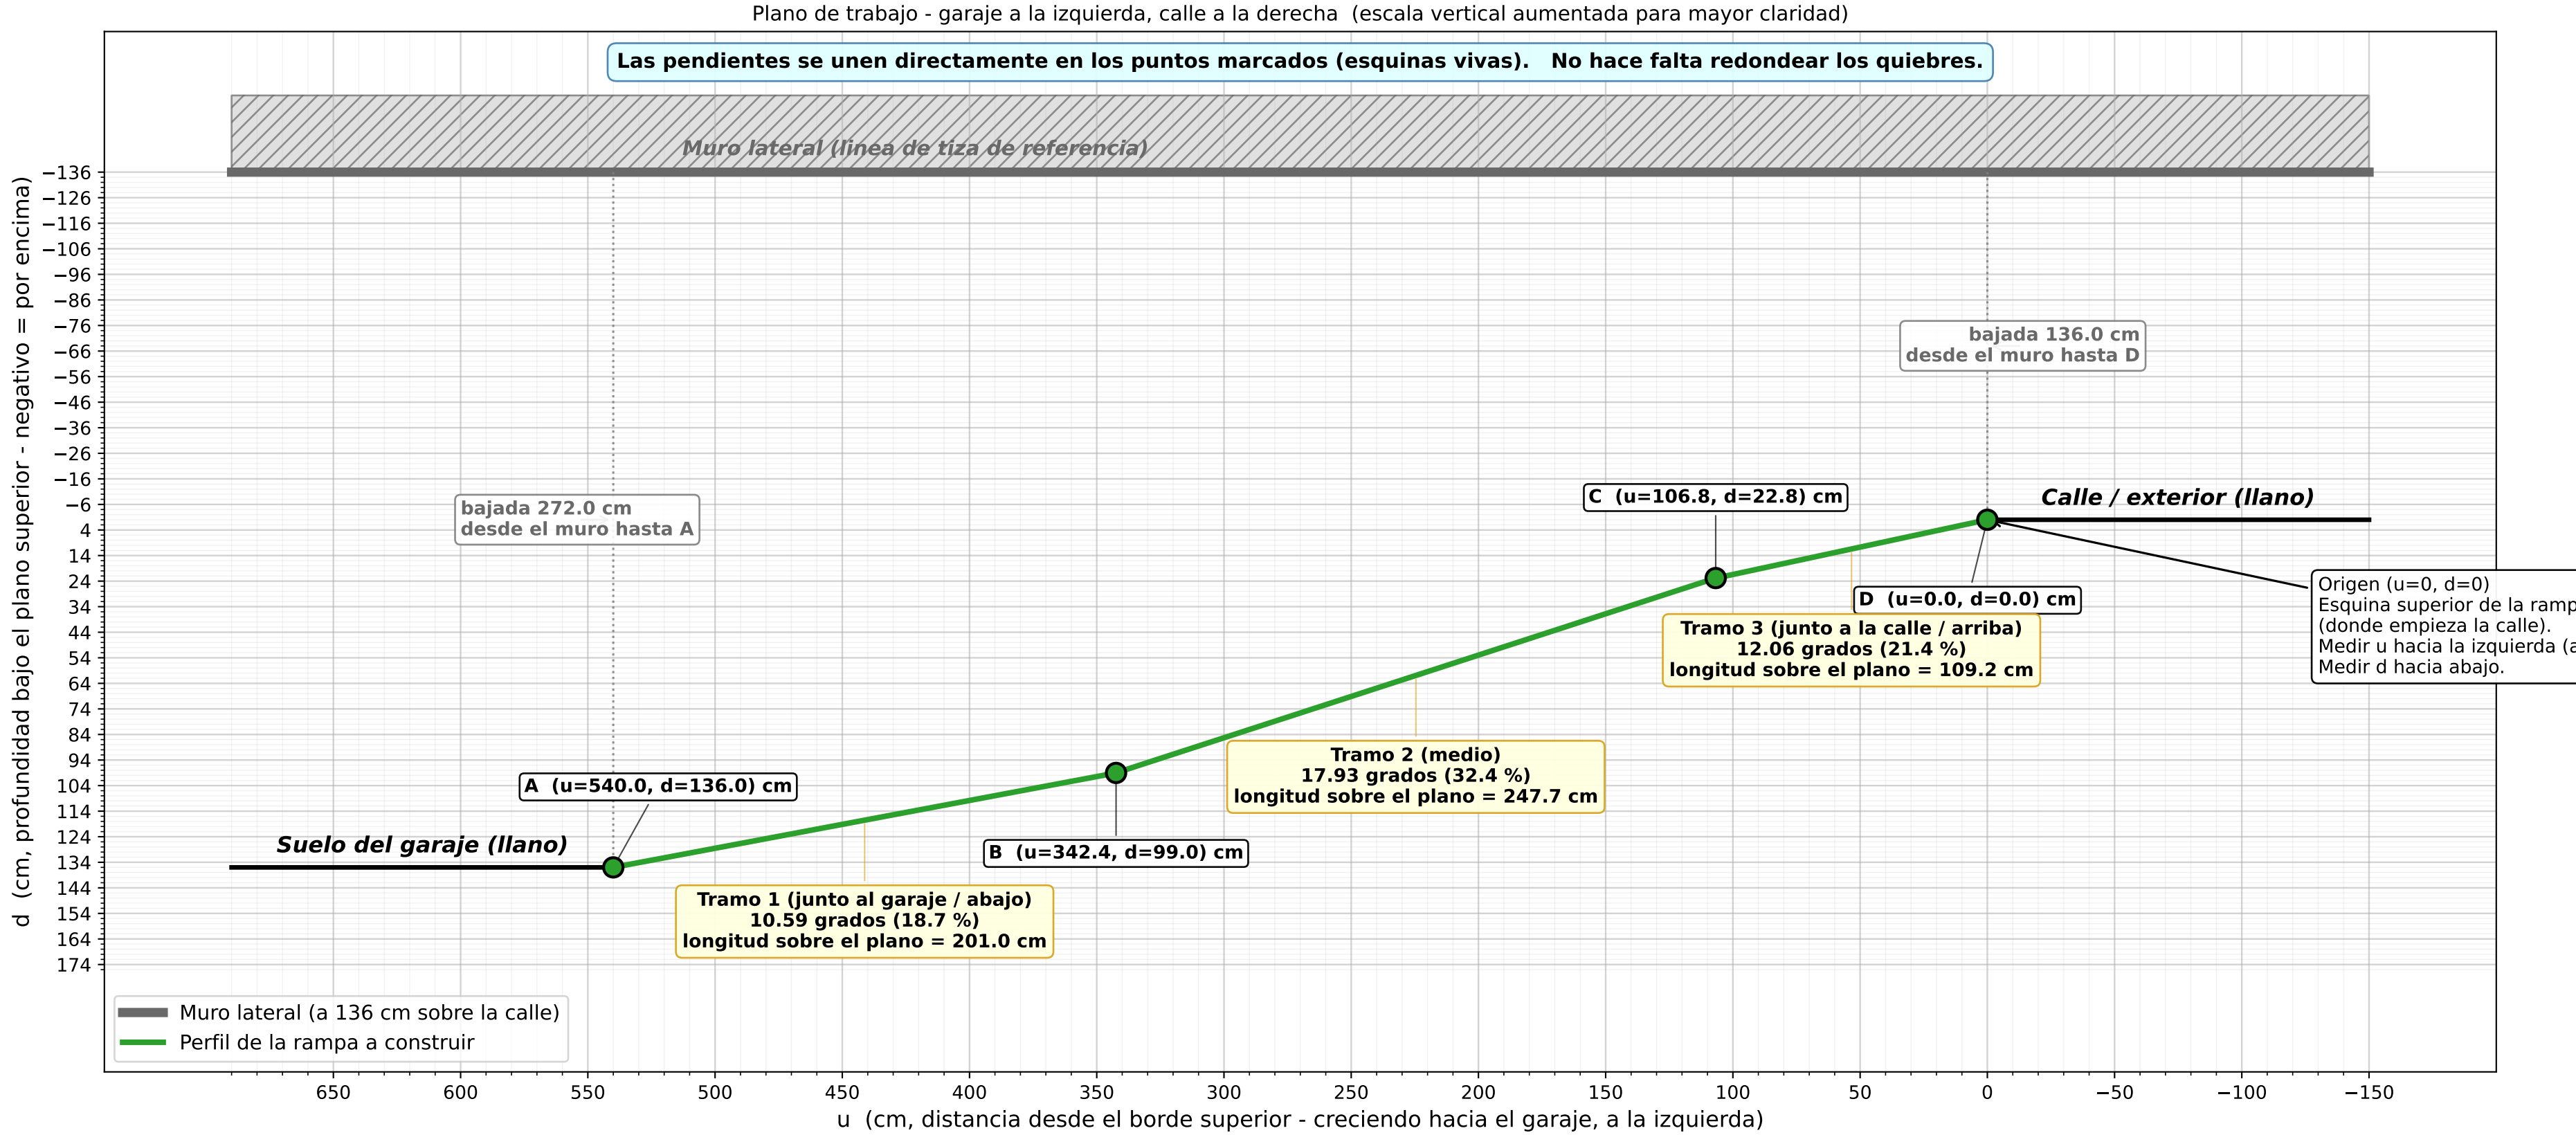

pt	que es	u (cm) hasta el borde superior	d (cm) bajo el plano superior	bajada (cm) desde el muro	tipo
A	Inicio de la rampa (esquina)	540.0	136.0	272.0	esquina
B	Quiebre 1 (esquina teorica)	342.4	99.0	235.0	esquina
C	Quiebre 2 (esquina teorica)	106.8	22.8	158.8	esquina
D	Fin de la rampa (esquina)	0.0	0.0	136.0	esquina