


Plano de construccion (referencia: muro y plano superior) - rampa de 4 tramos rectos (desnivel 136 cm, longitud 540 cm)

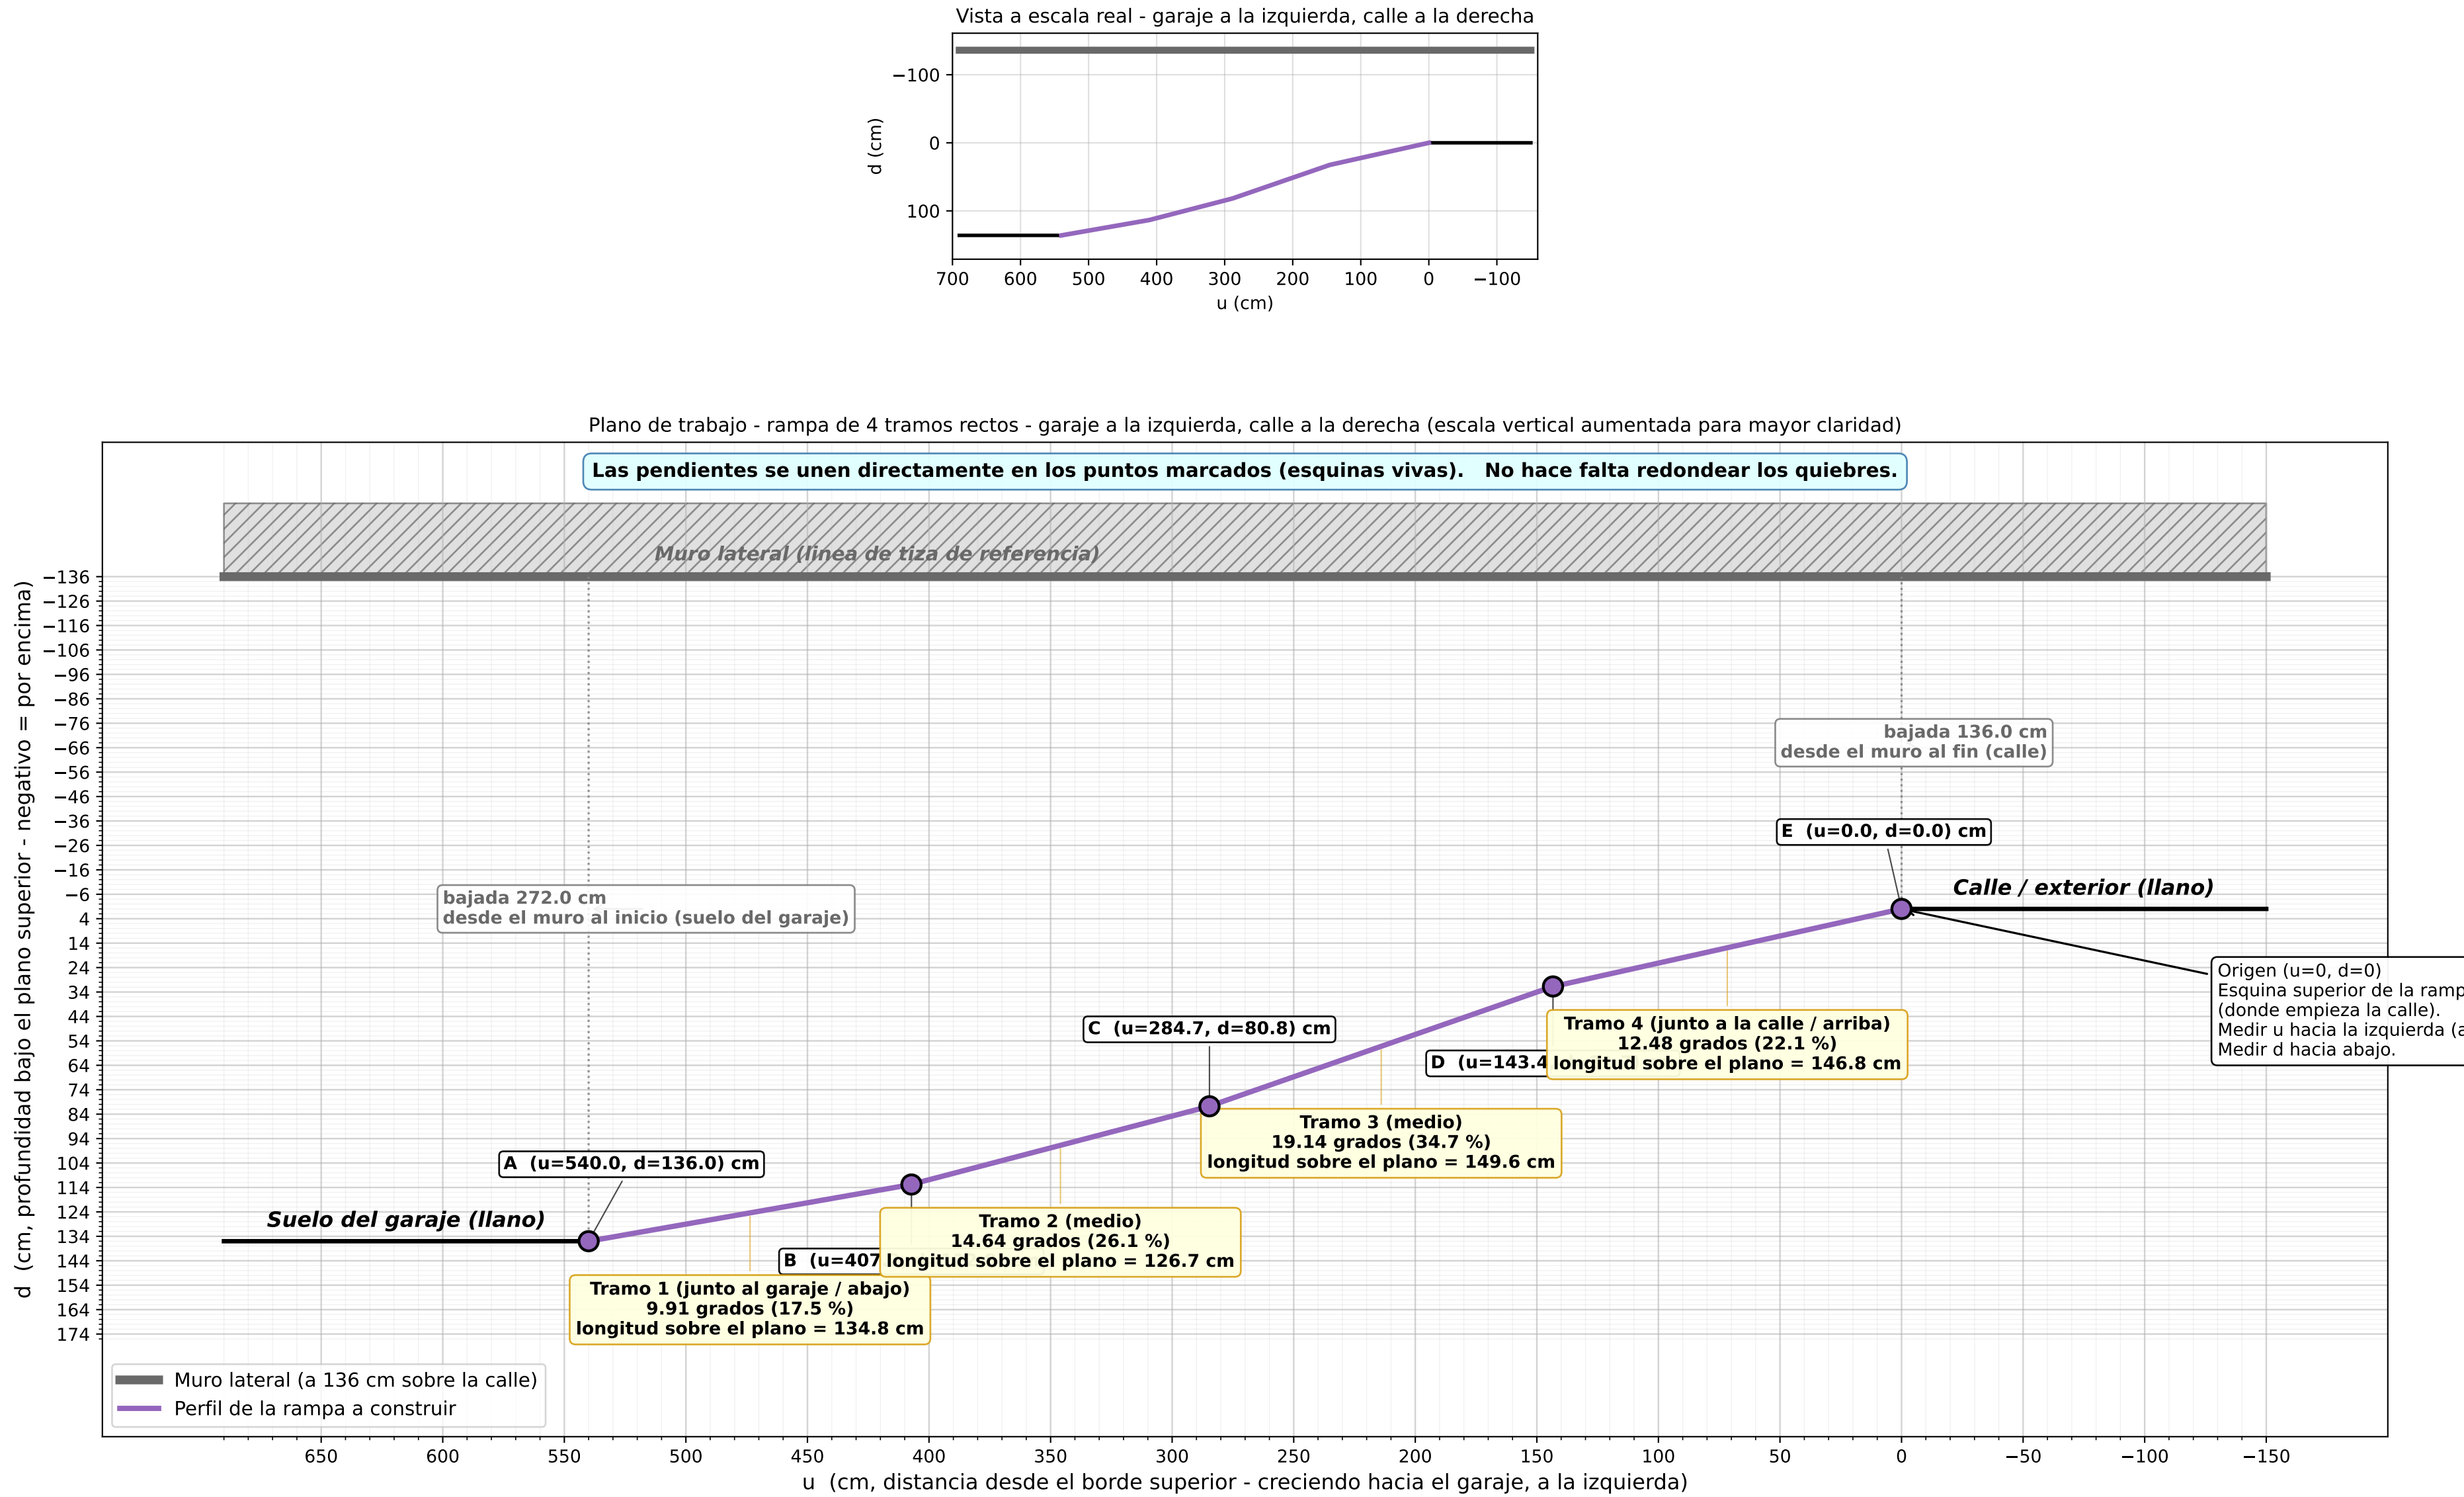

pt	que es	u (cm) hasta el borde superior	d (cm) bajo el plano superior	bajada (cm) desde el muro	tipo
A	Inicio de la rampa (junto al garaje)	540.0	136.0	272.0	esquina
B	Quiebre 1 (esquina)	407.2	112.8	248.8	esquina
C	Quiebre 2 (esquina)	284.7	80.8	216.8	esquina
D	Quiebre 3 (esquina)	143.4	31.7	167.7	esquina
E	Fin de la rampa (junto a la calle)	0.0	0.0	136.0	esquina