


Plano de construccion (referencia: muro y plano superior) - curva suave libre (PCHIP) (desnivel 136 cm, longitud 540 cm, estaciones cada 30 cm)

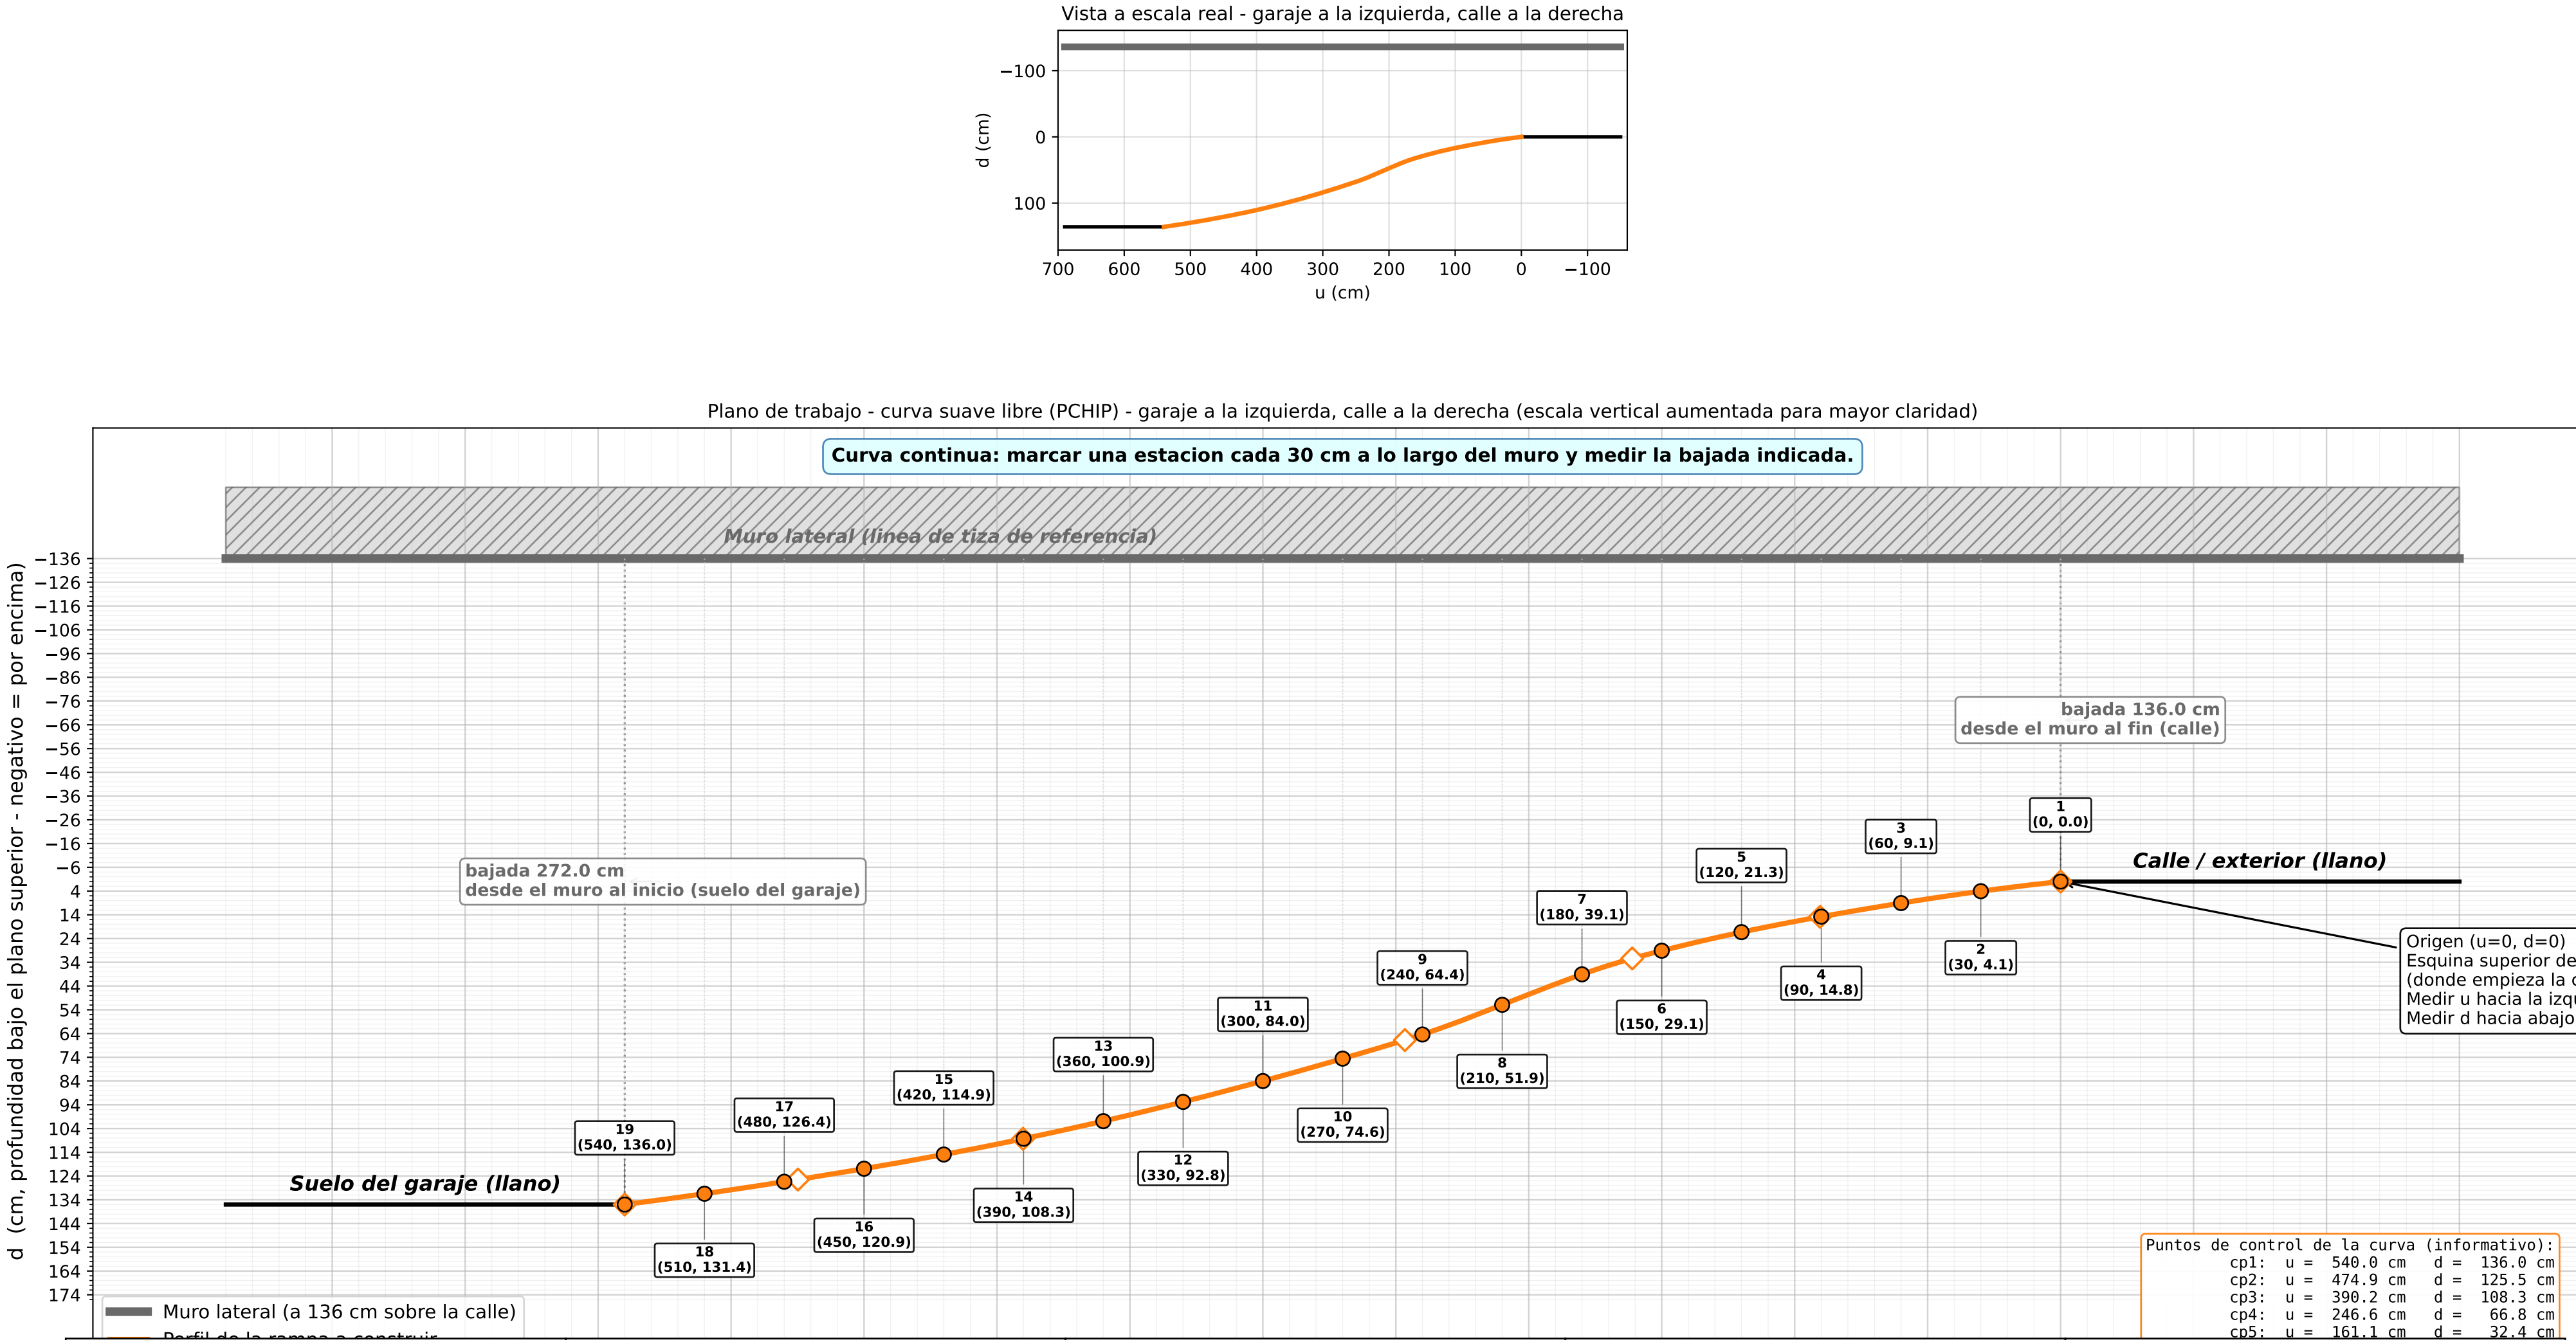

n	u (cm)	d (cm)	bajada (cm)	tipo
1	0.0	0.0	136.0	estacion superior (junto a la calle)
2	30.0	4.1	140.1	estacion intermedia
3	60.0	9.1	145.1	estacion intermedia
4	90.0	14.8	150.8	estacion intermedia
5	120.0	21.3	157.3	estacion intermedia
6	150.0	29.1	165.1	estacion intermedia
7	180.0	39.1	175.1	estacion intermedia
8	210.0	51.9	187.9	estacion intermedia
9	240.0	64.4	200.4	estacion intermedia
10	270.0	74.6	210.6	estacion intermedia
11	300.0	84.0	220.0	estacion intermedia
12	330.0	92.8	228.8	estacion intermedia
13	360.0	100.9	236.9	estacion intermedia
14	390.0	108.3	244.3	estacion intermedia
15	420.0	114.9	250.9	estacion intermedia
16	450.0	120.9	256.9	estacion intermedia
17	480.0	126.4	262.4	estacion intermedia
18	510.0	131.4	267.4	estacion intermedia
19	540.0	136.0	272.0	estacion inferior (junto al garaie)